


LEGEND

- MONUMENT FOUND AS LABELED
- ∅ UTILITY POLE
- + UTILITY POLE ANCHOR
- CPP CORRUGATED PLASTIC PIPE
- - - - - EDGE OF TRAVELED WAY
- x - WOODEN STOCKADE FENCE
- - - - - OVERHEAD WIRES
- - - - - EDGE OF RIGHT OF WAY
- — — — — PROPERTY LINE
- >— DITCH

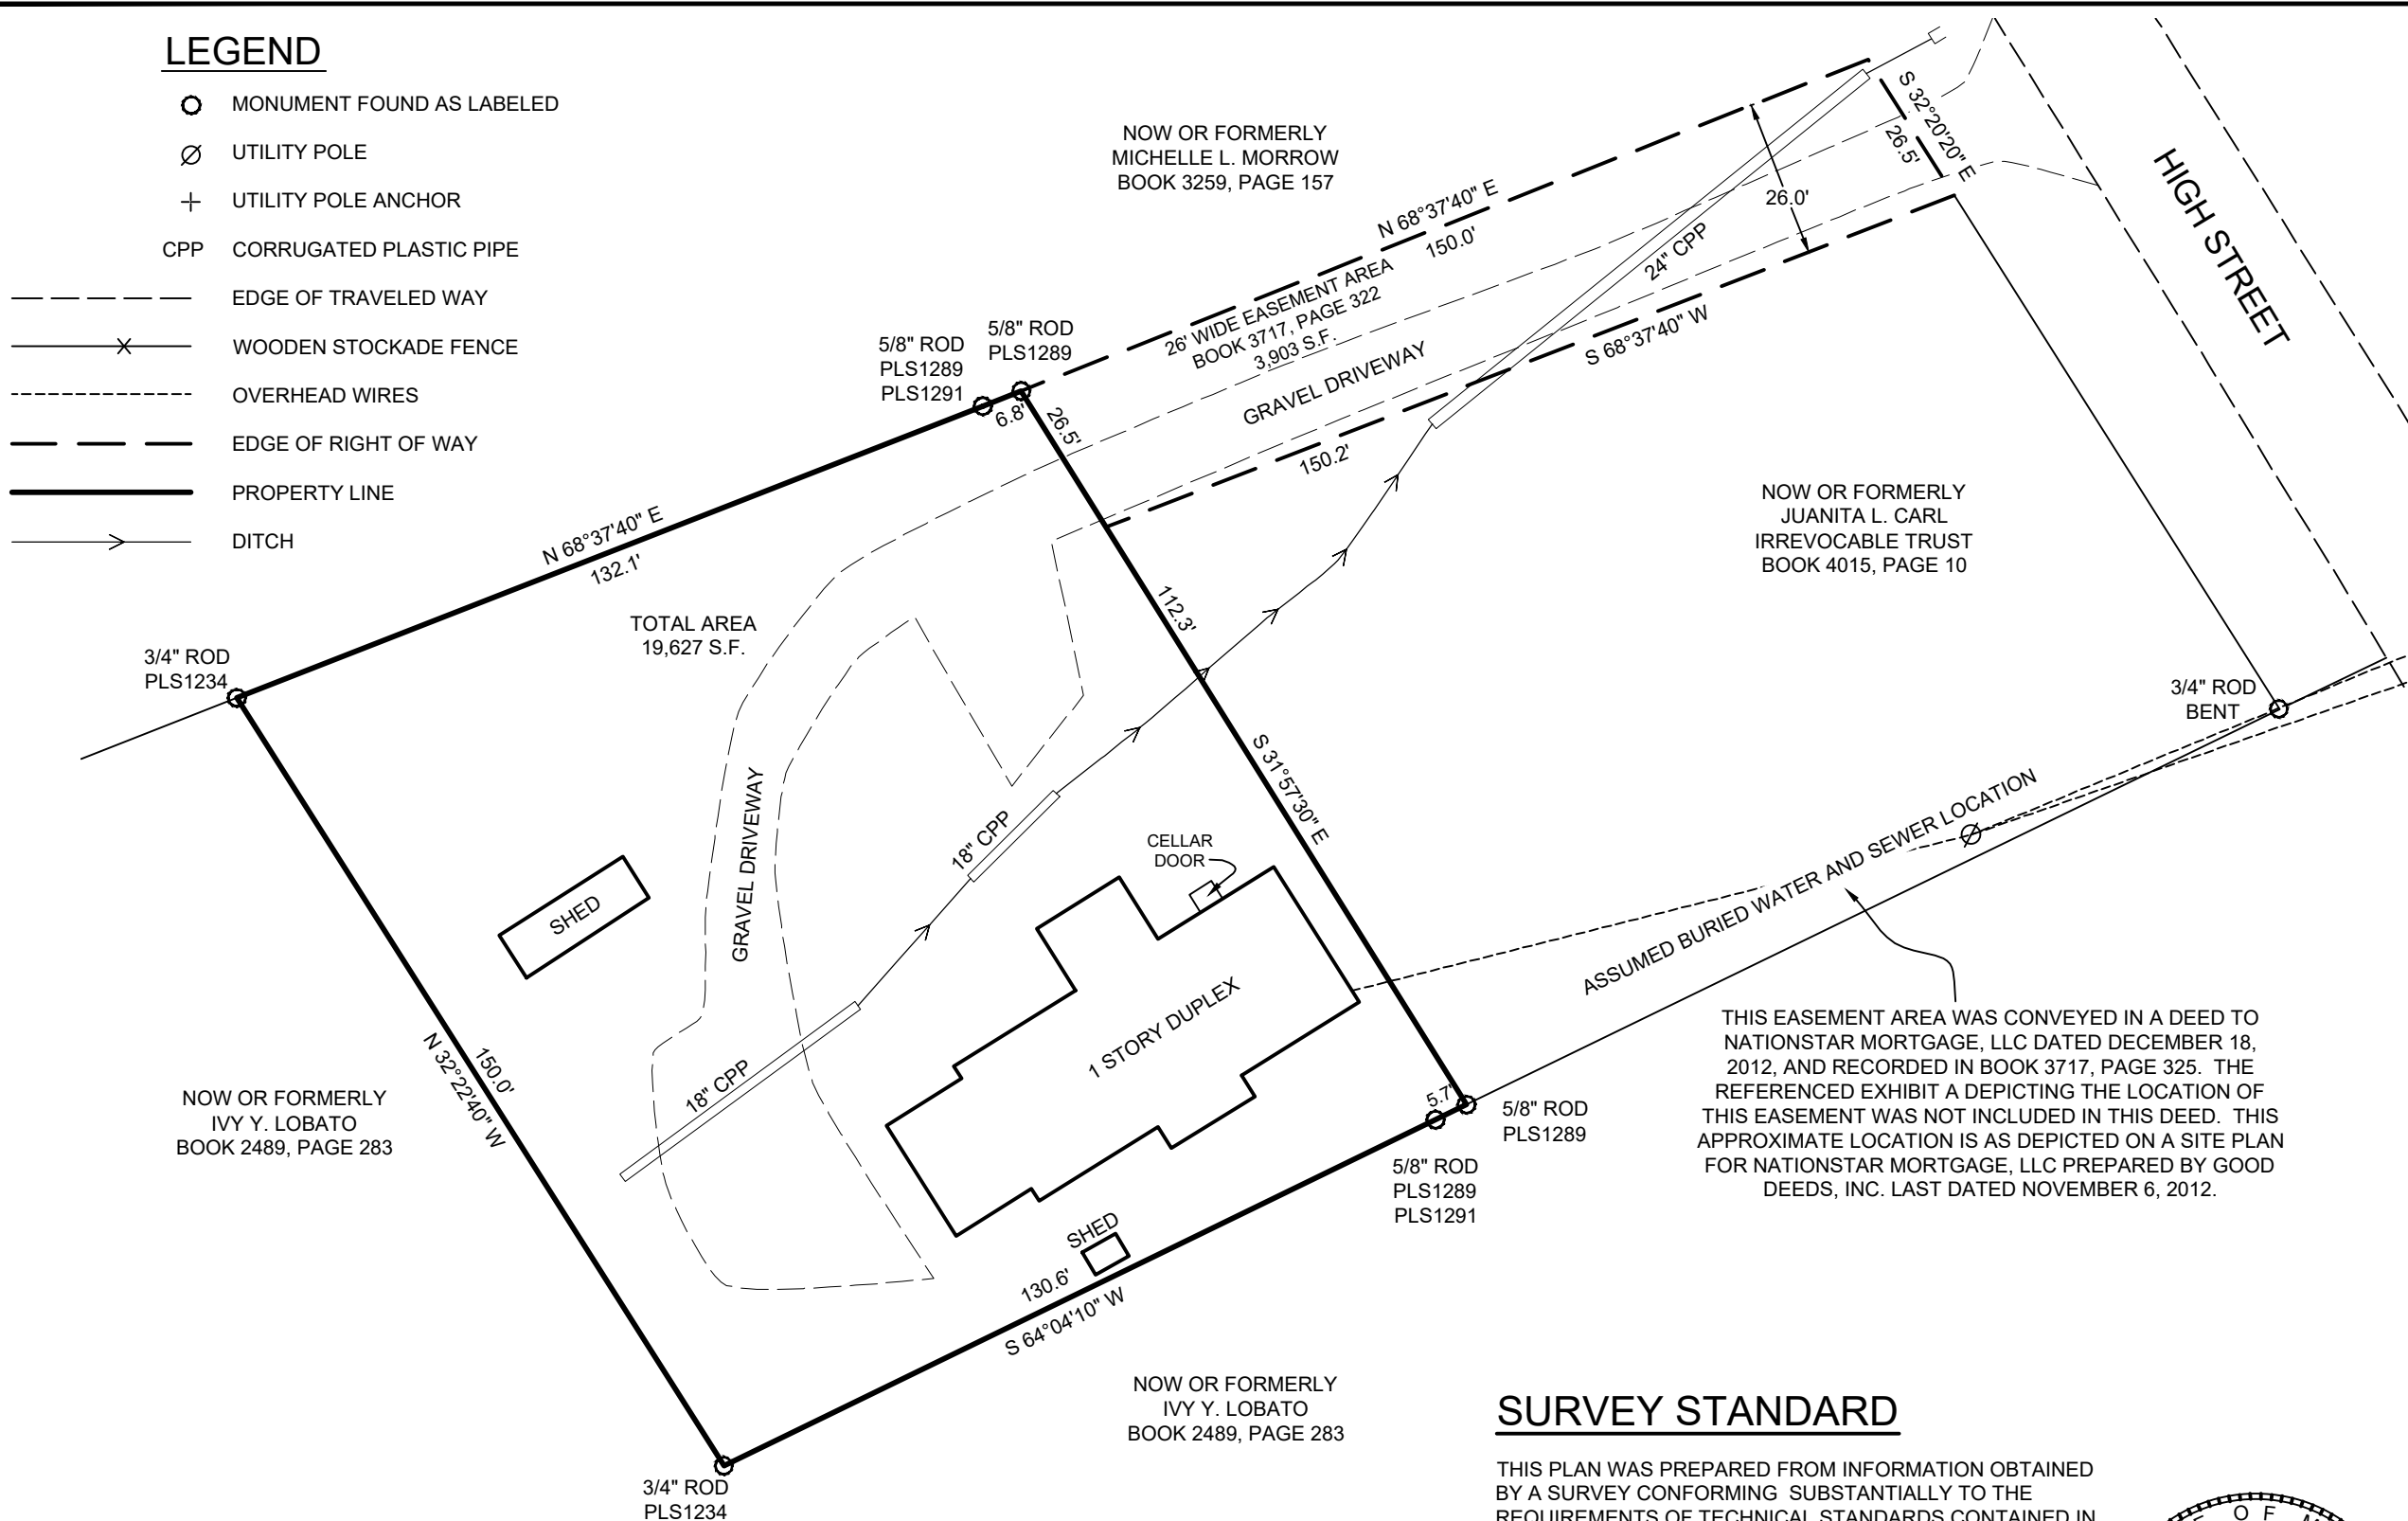

NOW OR FORMERLY
IVY Y. LOBATO
BOOK 2489, PAGE 283

NOW OR FORMERLY
MICHELLE L. MORROW
BOOK 3259, PAGE 157

NOW OR FORMERLY
JUANITA L. CARL
IRREVOCABLE TRUST
BOOK 4015, PAGE 10



NOW OR FORMERLY
IVY Y. LOBATO
BOOK 2489, PAGE 283

SURVEY STANDARD


THIS PLAN WAS PREPARED FROM INFORMATION OBTAINED BY A SURVEY CONFORMING SUBSTANTIALLY TO THE REQUIREMENTS OF TECHNICAL STANDARDS CONTAINED IN CHAPTER 90, PART 2, OF THE RULES OF THE BOARD OF LICENSURE FOR PROFESSIONAL LAND SURVEYORS, EFFECTIVE APRIL 1, 2001.

Clark G. Staples

CLARK G. STAPLES, MAINE LICENSED
PROFESSIONAL LAND SURVEYOR No. 2332

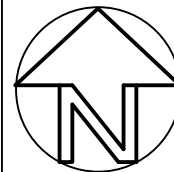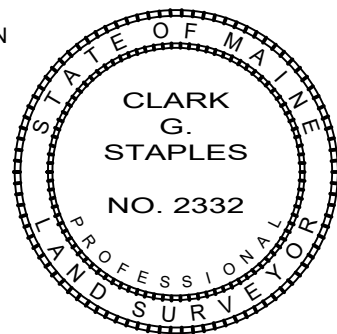

MAINE COORDINATE
SYSTEM OF 1983
EAST ZONE
(2011)(EPOCH:2010.0000)

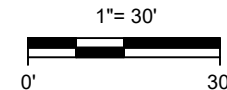

NOTES:

- (1) DOCUMENTS REFERENCED ON THIS PLAN ARE RECORDED IN THE WALDO COUNTY REGISTRY OF DEEDS UNLESS OTHERWISE NOTED.
- (2) NO SURVEYOR'S REPORT WAS PREPARED.
- (3) BUILDING FOOTPRINTS AND LOCATIONS ARE BASED ON DRAWINGS PROVIDED BY OWNER.

BOUNDARY SURVEY
LANDS OF
ROBERT L. MORRISON

358 HIGH STREET
WALDO COUNTY REGISTRY OF DEEDS
BOOK 4955, PAGE 182
BOOK 5022, PAGE 308

GOOD DEEDS



LAND SURVEYING • DEED RESEARCH

P.O. BOX 587 109 MAIN STREET BELFAST, ME 04915 (207) 338-5743	PROJ. 24039 DATE: 5-29-2025
--	--------------------------------