


LOCATION1	LOCATION2	SCOPE DESCRIPTION
UNIT 1		RELOCATE ELECTRIC SERVICE OUTWARD BY 4 INCHES. INSTALL NEW 2.5" CONDUIT RISER AND REUSE EXISTING RISER FOR LV UTILITIES
UNIT 1	SEE DRAWINGS	ADD ELECTRIC HEAT CIRCUIT FOR BACKUP HEAT STRIPS (EFTR) AND AHU REHEAT (RHC) AS SHOWN ON DRAWINGS. HEAT STRIPS WITH INTEGRAL THERMOSTATS
UNIT 1	CRAWL SPACE	FURNISH AND INSTALL DISCONNECT FOR DUCT HEAT PUMP INDOOR UNIT LOCATED IN CRAWL SPACE
UNIT 1		ADD SURFACE MOUNTED KITCHEN EXHAUST FAN
UNIT 1	SEE DRAWINGS	FURNISH AND INSTALL DISCONNECT FOR SINGLE ZONE HEAT PUMP OUTDOOR UNIT, UNIT LOCATION TBD
UNIT 1	NEW MECH/ STORAGE ROOM 1	INSTALL DISCONNECT FOR HEAT PUMP WATER HEATER, REUSE 30A DISCONNECT
UNIT 1	MUDROOM 1	FURNISH 30A, 2P WASHER/DRYER RECEPTICLE IN NEW MUDROOM
UNIT 1	MUDROOM 1	REMOVE EXISTING GFI OUTDOOR RECEPTICLE ON NORTH SIDE
UNIT 1	ALL ROOMS	REPLACE ALL EXISTING INDOOR RECEPTICLES WITH TAMPER PROOF, NEW SWITCH COVERS (WHITE, STANDARD), APPROXIMATE COUNT OF 25
UNIT 1		REPLACE OUTDOOR RECEPTICLE ON SOUTH SIDE
UNIT 1		ADD NEW OUTDOOR RECEPTICLES, NEW ENTRY, NEW STORAGE ROOM
UNIT 1	NEW BATHROOM 1-2	ADD RECEPTICLE FOR NEW BATHROOM
UNIT 1	SEE DRAWINGS	ADD NEW LIGHTING FIXTURES, 6" RAZOR, APPROXIMATE COUNT 25. ADD NEW DIMMER SWITCHES (NON DECORA) IN EXISTING SWITCH BOXES
UNIT 1		EXISTING BATHROOM EXHAUST FAN TO BE REMOVED
UNIT 1	BATHROOM 1-1	REPLACE BATHROOM VANITY LIGHT FIXTURES
UNIT 1		REPLACE OUTSIDE FIXTURE ON SOUTH ENTRY
UNIT 1		ADD NEW HIGH ENDWALL OUTDOOR FIXTURES ON END WALLS
UNIT 1		ADD MEANS FOR FUTURE 50 A, 2P, OUTDOOR RECEPTICAL FOR VEHICLE CHARGER
UNIT 2		RELOCATE ELECTRIC SERVICE OUTWARD BY 4 INCHES. INSTALL NEW 2.5" CONDUIT RISER AND REUSE EXISTING RISER FOR LV UTILITIES
UNIT 2	SEE DRAWINGS	ADD ELECTRIC HEAT CIRCUIT FOR BACKUP HEAT STRIPS (EFTR) AND AHU REHEAT (RHC) AS SHOWN ON DRAWINGS. HEAT STRIPS WITH INTEGRAL THERMOSTATS
UNIT 2	CRAWL SPACE	FURNISH AND INSTALL DISCONNECT FOR DUCT HEAT PUMP INDOOR UNIT LOCATED IN CRAWL SPACE
UNIT 2		ADD SURFACE MOUNTED KITCHEN EXHAUST FAN
UNIT 2	SEE DRAWINGS	FURNISH AND INSTALL DISCONNECT FOR SINGLE ZONE HEAT PUMP OUTDOOR UNIT, UNIT LOCATION TBD
UNIT 2	NEW MECH/ STORAGE ROOM 2	INSTALL DISCONNECT FOR HEAT PUMP WATER HEATER, REUSE 30A DISCONNECT
UNIT 2	MUDROOM 2	FURNISH 30A, 2P WASHER/DRYER RECEPTICLE IN NEW MUDROOM
UNIT 2	MUDROOM 2	REMOVE EXISTING GFI OUTDOOR RECEPTICLE ON NORTH SIDE
UNIT 2	ALL ROOMS	REPLACE ALL EXISTING INDOOR RECEPTICLES WITH TAMPER PROOF, NEW SWITCH COVERS (WHITE, STANDARD), APPROXIMATE COUNT OF 25
UNIT 2		REPLACE OUTDOOR RECEPTICLE ON SOUTH SIDE
UNIT 2		ADD NEW OUTDOOR RECEPTICLES, NEW ENTRY, NEW STORAGE ROOM
UNIT 2	NEW BATHROOM 2-2	ADD RECEPTICLE FOR NEW BATHROOM
UNIT 2	SEE DRAWINGS	ADD NEW LIGHTING FIXTURES, 6" RAZOR, APPROXIMATE COUNT 25. ADD NEW DIMMER SWITCHES (NON DECORA) IN EXISTING SWITCH BOXES
UNIT 2		EXISTING BATHROOM EXHAUST FAN TO BE REMOVED
UNIT 2	BATHROOM 2-1	REPLACE BATHROOM VANITY LIGHT FIXTURES
UNIT 2		REPLACE OUTSIDE FIXTURE ON SOUTH ENTRY
UNIT 2		ADD NEW HIGH ENDWALL OUTDOOR FIXTURES ON END WALLS
UNIT 2		ADD MEANS FOR FUTURE 50 A, 2P, OUTDOOR RECEPTICAL FOR VEHICLE CHARGER

SCOPE OF WORK

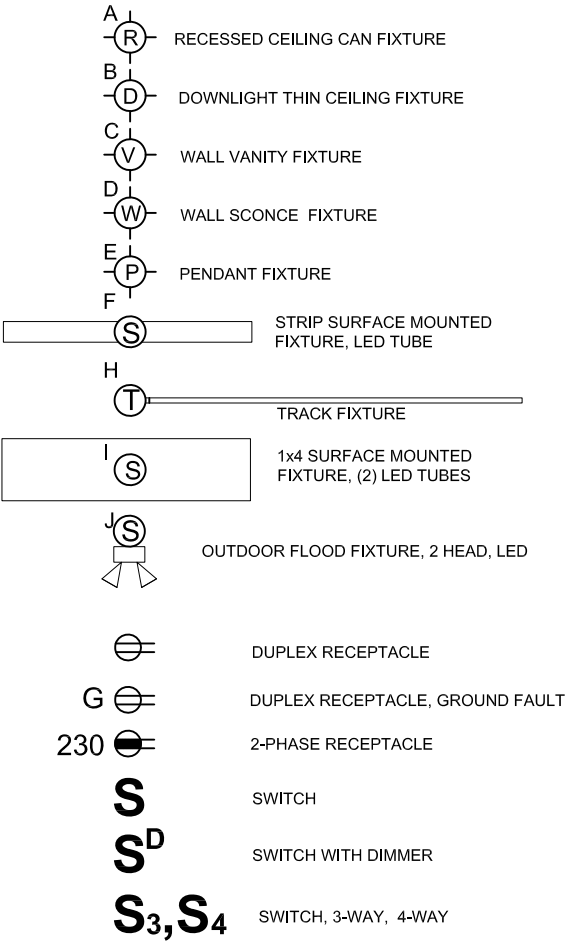


PROGRESS

https://358highstreet.com
<i>Owners</i> Deborah Wolozin, Robert Morrison Palermo, ME 04354
<i>General Contractor</i> NORTHBRIDGE CONSTRUCTION 1774 North Union Rd. Union, ME 04862 207-593-6089
<i>HVAC Design and Implementation</i> OCTOBER ENGINEERING LLC Palermo, ME 04354 207-649-0505
ENERGY RETROFIT AND ELECTRIFICATION 358 High Street Belfast, ME 04915

SCOPE OF WORK

06-13-2024	E-1 1 of 3
------------	----------------------

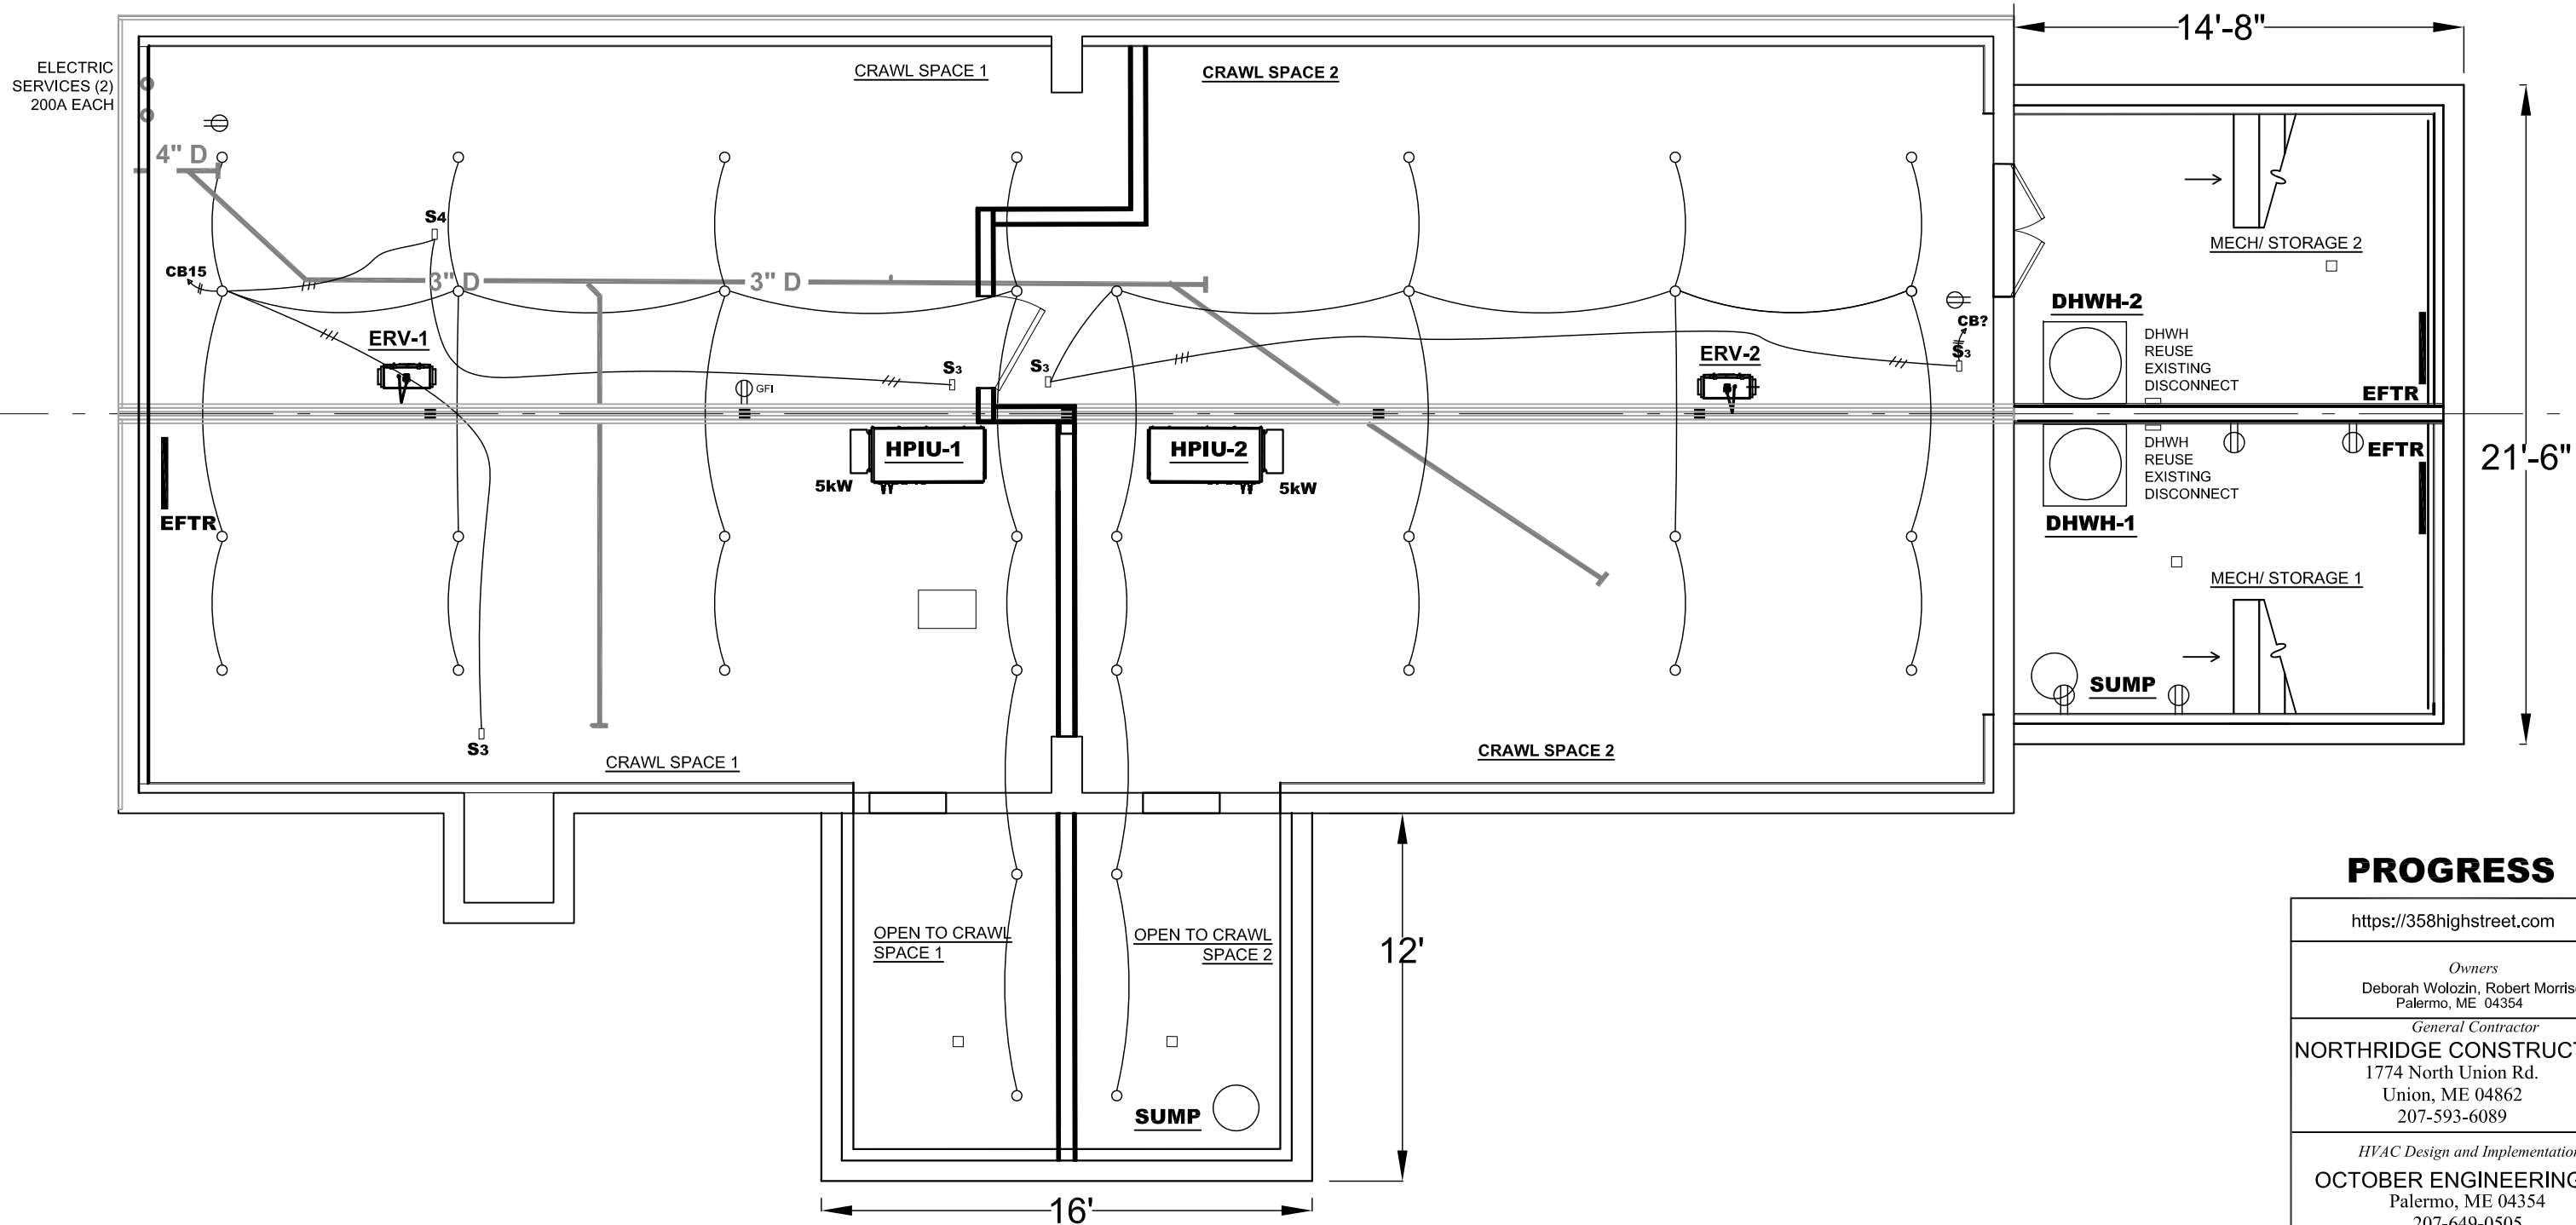

CRAWL SPACE FLOOR PLAN

SCALE: $\frac{3}{16}" = 1'0"$ (11x17)

PROGRESS

<https://358highstreet.com>

Owners
Deborah Wolozin, Robert Morrison
Palermo, ME 04354

General Contractor
NORTHBRIDGE CONSTRUCTION
1774 North Union Rd.
Union, ME 04862
207-593-6089


HVAC Design and Implementation
OCTOBER ENGINEERING LLC
Palermo, ME 04354
207-649-0505

**ENERGY RETROFIT AND
ELECTRIFICATION**
358 High Street
Belfast, ME 04915

CRAWL SPACE PLAN

06-13-2024

E-2
2 of 3

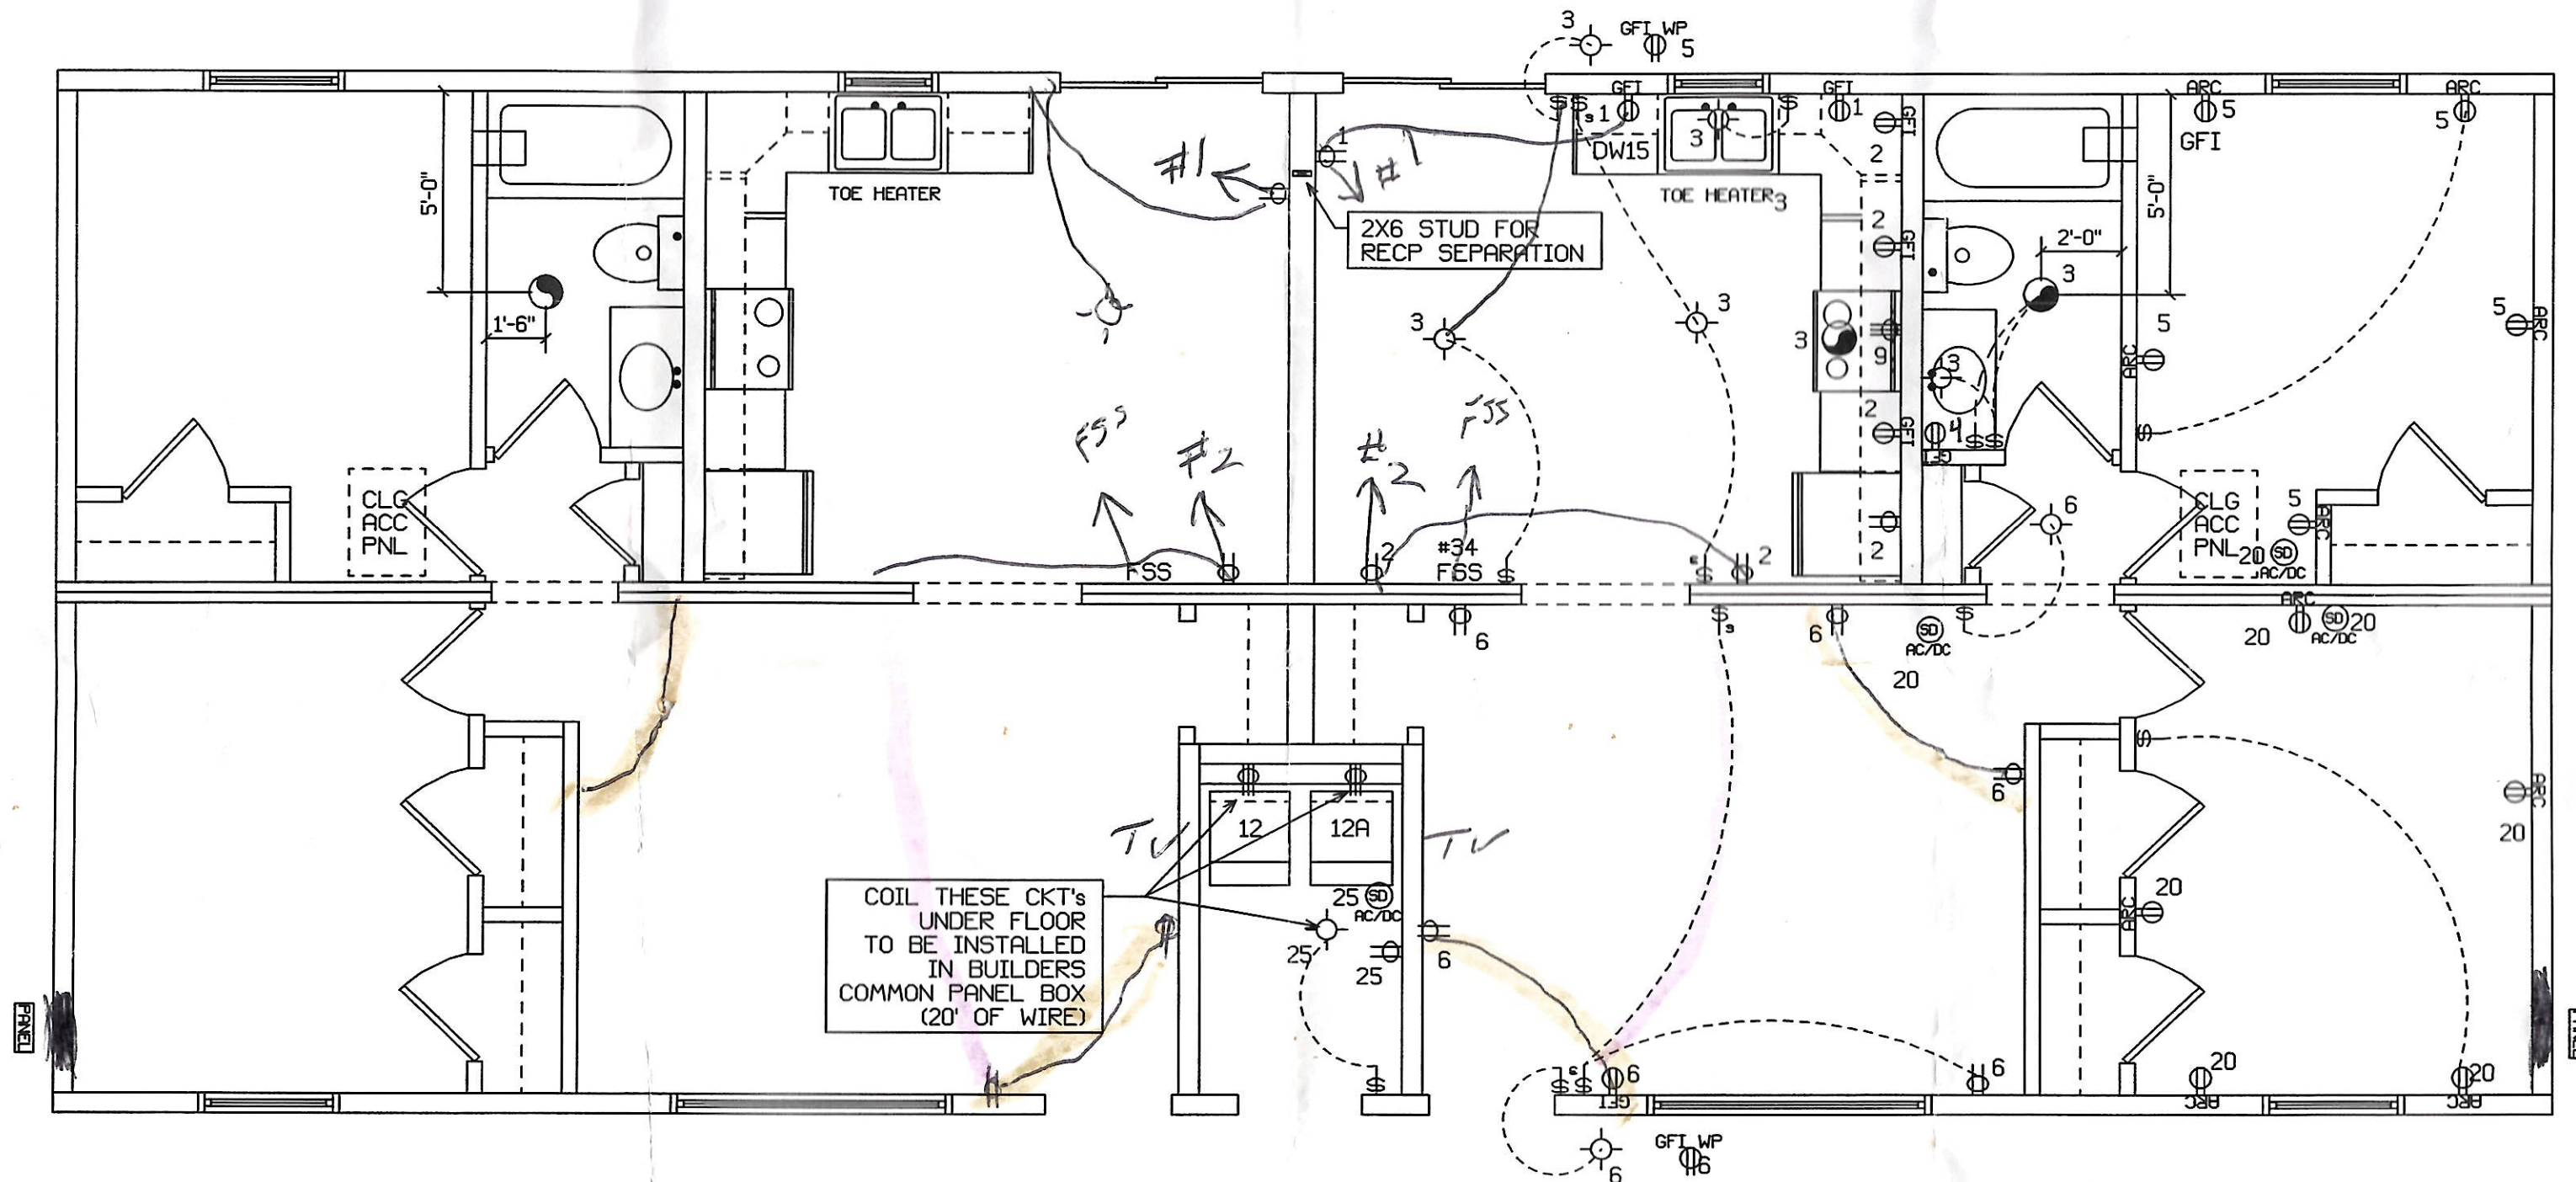

HOLD BACK GYPBD 1'-0" PER SIDE IN OPEN AREAS
 STAIRS DESIGNED TO 8 1/4" RISE MAX. AND 9" TREAD MIN W/ 1 1/8" NOSING

Bldr/DEVL. AUTHORIZATION	DATE	# LABEL LOCATION	Linda A. Litz LINDA A. LITZ PRODUCTION ENGINEER	GJH 7/21/2004 #788	REV.
MANUF. AUTHORIZATION	DATE	THIS PLAN DERIVED FROM MASTER SERIES BUILDING SYSTEM	1565 PA. RT. 442 E. MUNCY, PA. 17756 A DIVISION OF MUNCY HOMES, INC.	7919788p	
		DWN BY	DATE 5-20-04	SCALE 1/4"=1'-0"	ELECTRICAL PLAN