

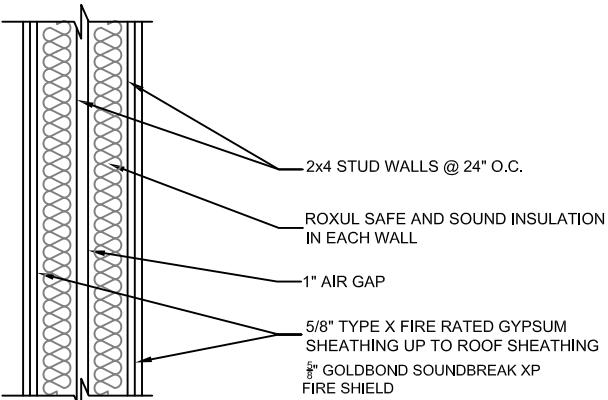


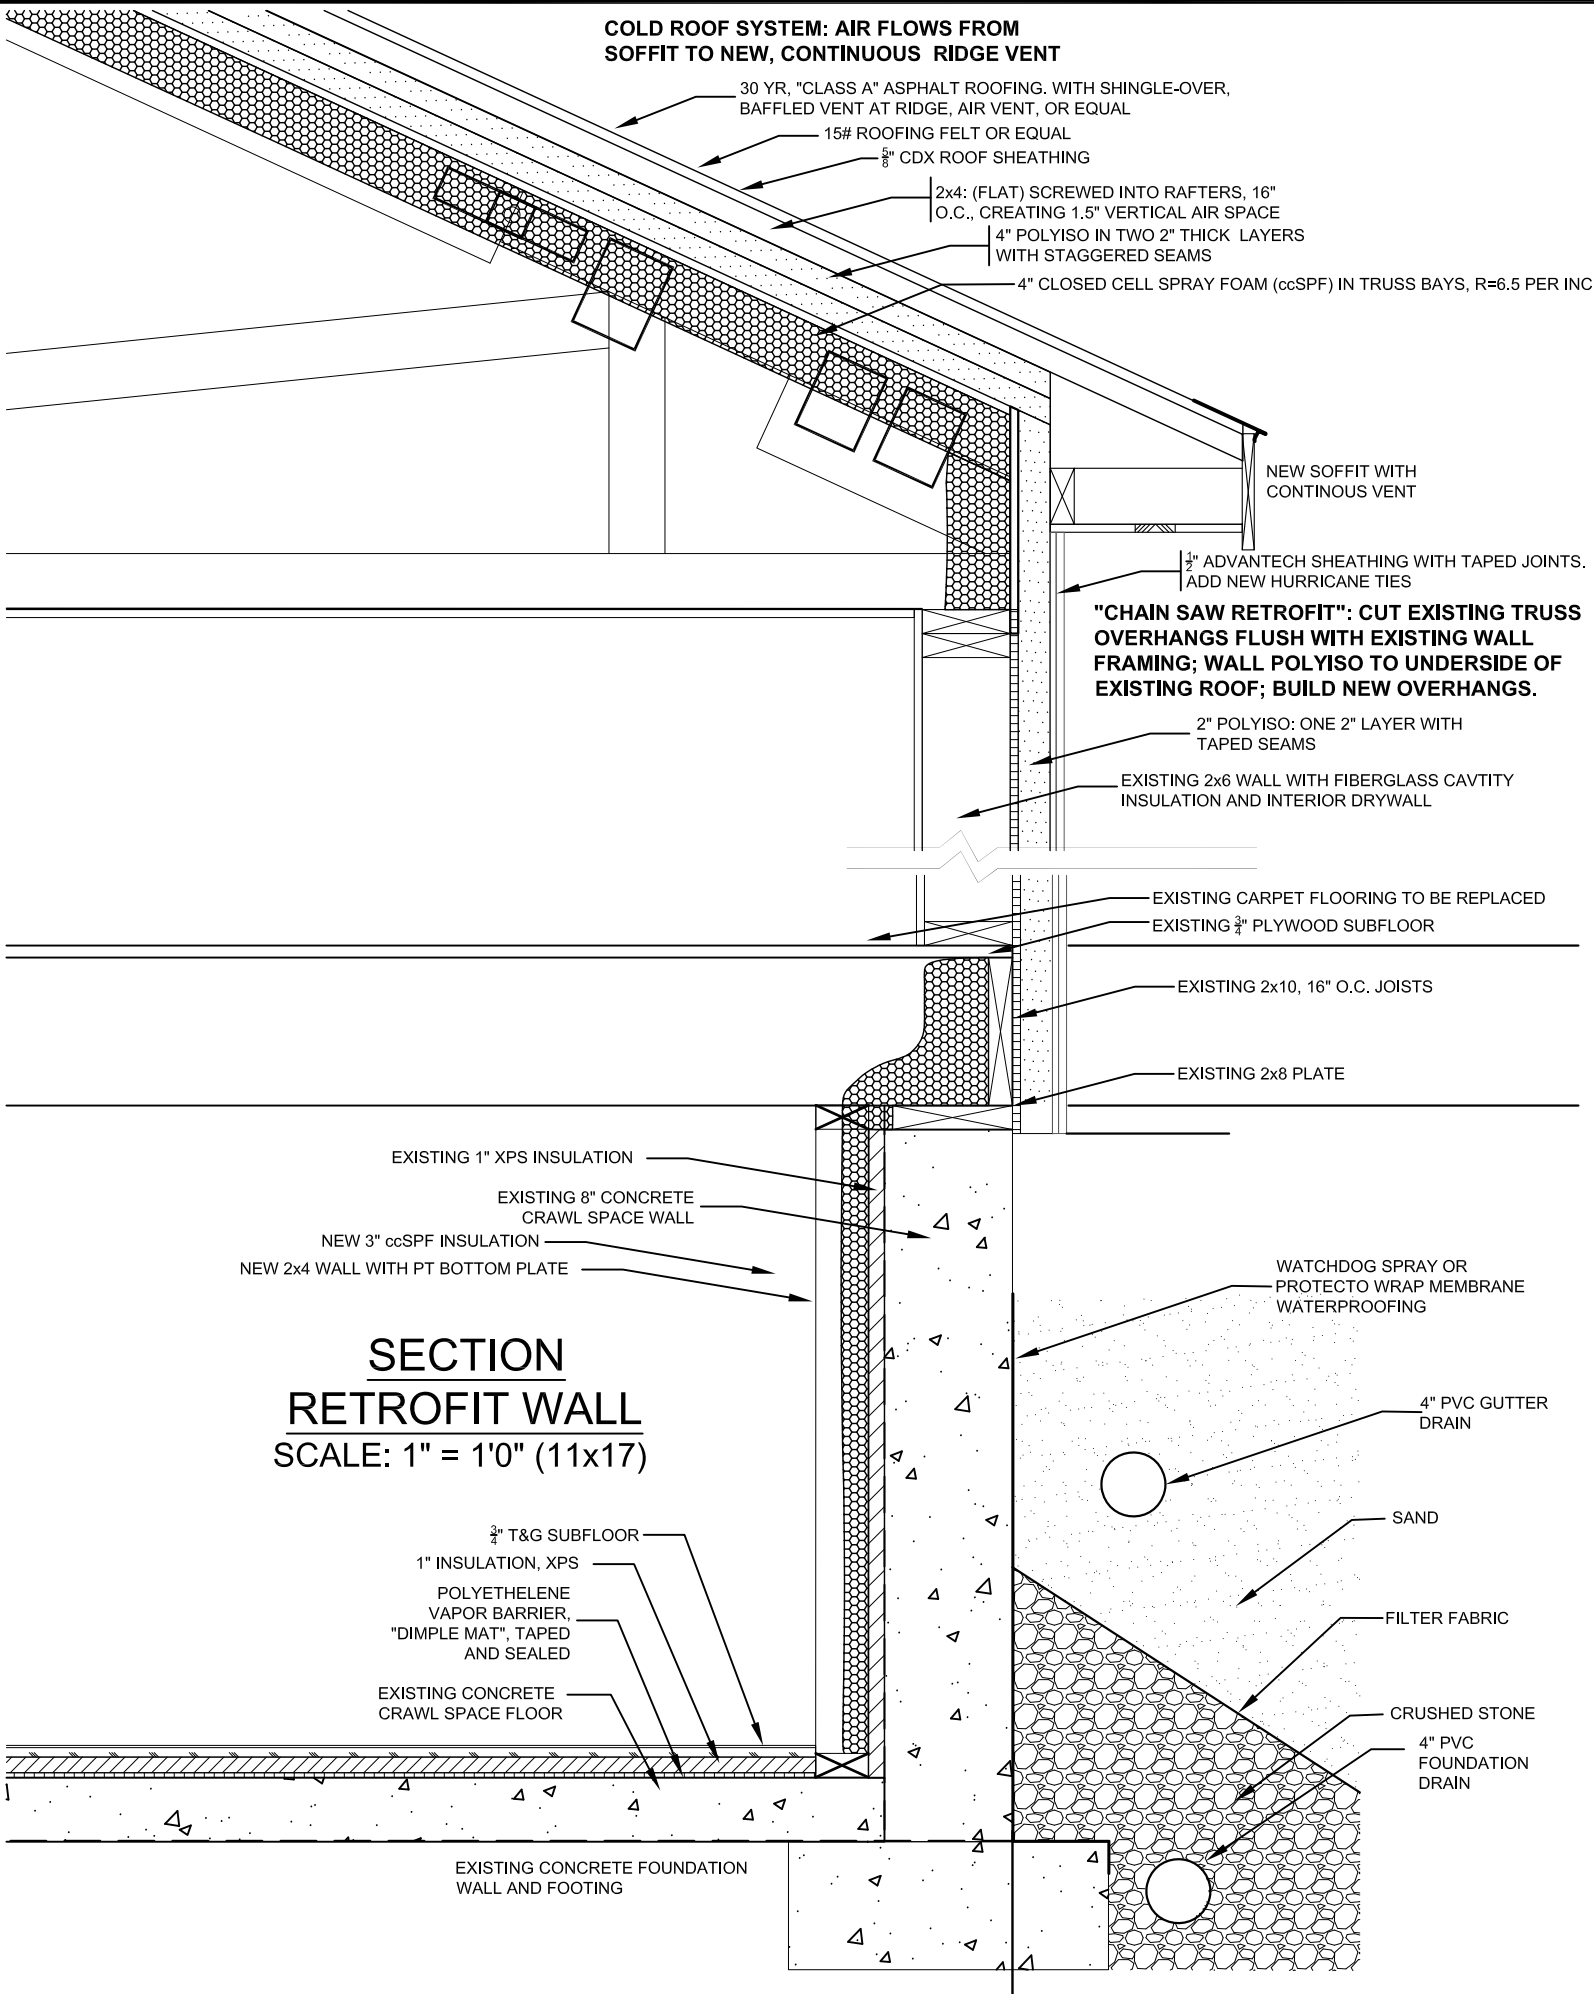


ONE HOUR FIRE AND SOUND SEPARATION

FIRE SEPARATION WALL #1

NTS

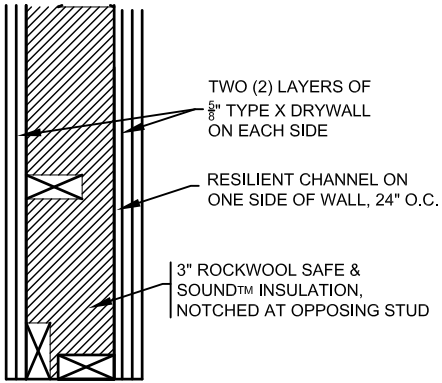

TOP VIEW

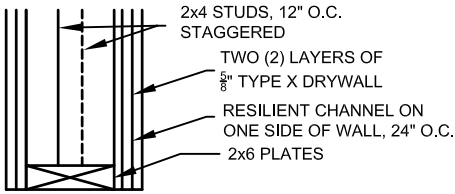

SIDE VIEW

ROCKWOOL ASSEMBLY IWS-354

FIRE SEPARATION WALL #2A

SCALE: 1" = 1'0" (11x17)

**FIRE SEPARATION WALL #2B:
SAME AS 2A WITHOUT CHANNEL**

https://358highstreet.com	
<i>Owners</i> Deborah Wolozin, Robert Morrison Palermo, ME 04354	
<i>General Contractor</i> NORTHEDGE CONSTRUCTION Mike Martin 1774 North Union Rd. Union, ME 04862 207-593-6089	
<i>HVAC Design and Implementation</i> OCTOBER ENGINEERING LLC Palermo, ME 04354 207-649-0505	
ENERGY RETROFIT AND ELECTRIFICATION 358 High Street Belfast, ME 04915	
PROPOSED SECTIONS	
08-18-2024	A-9 9 of 12